


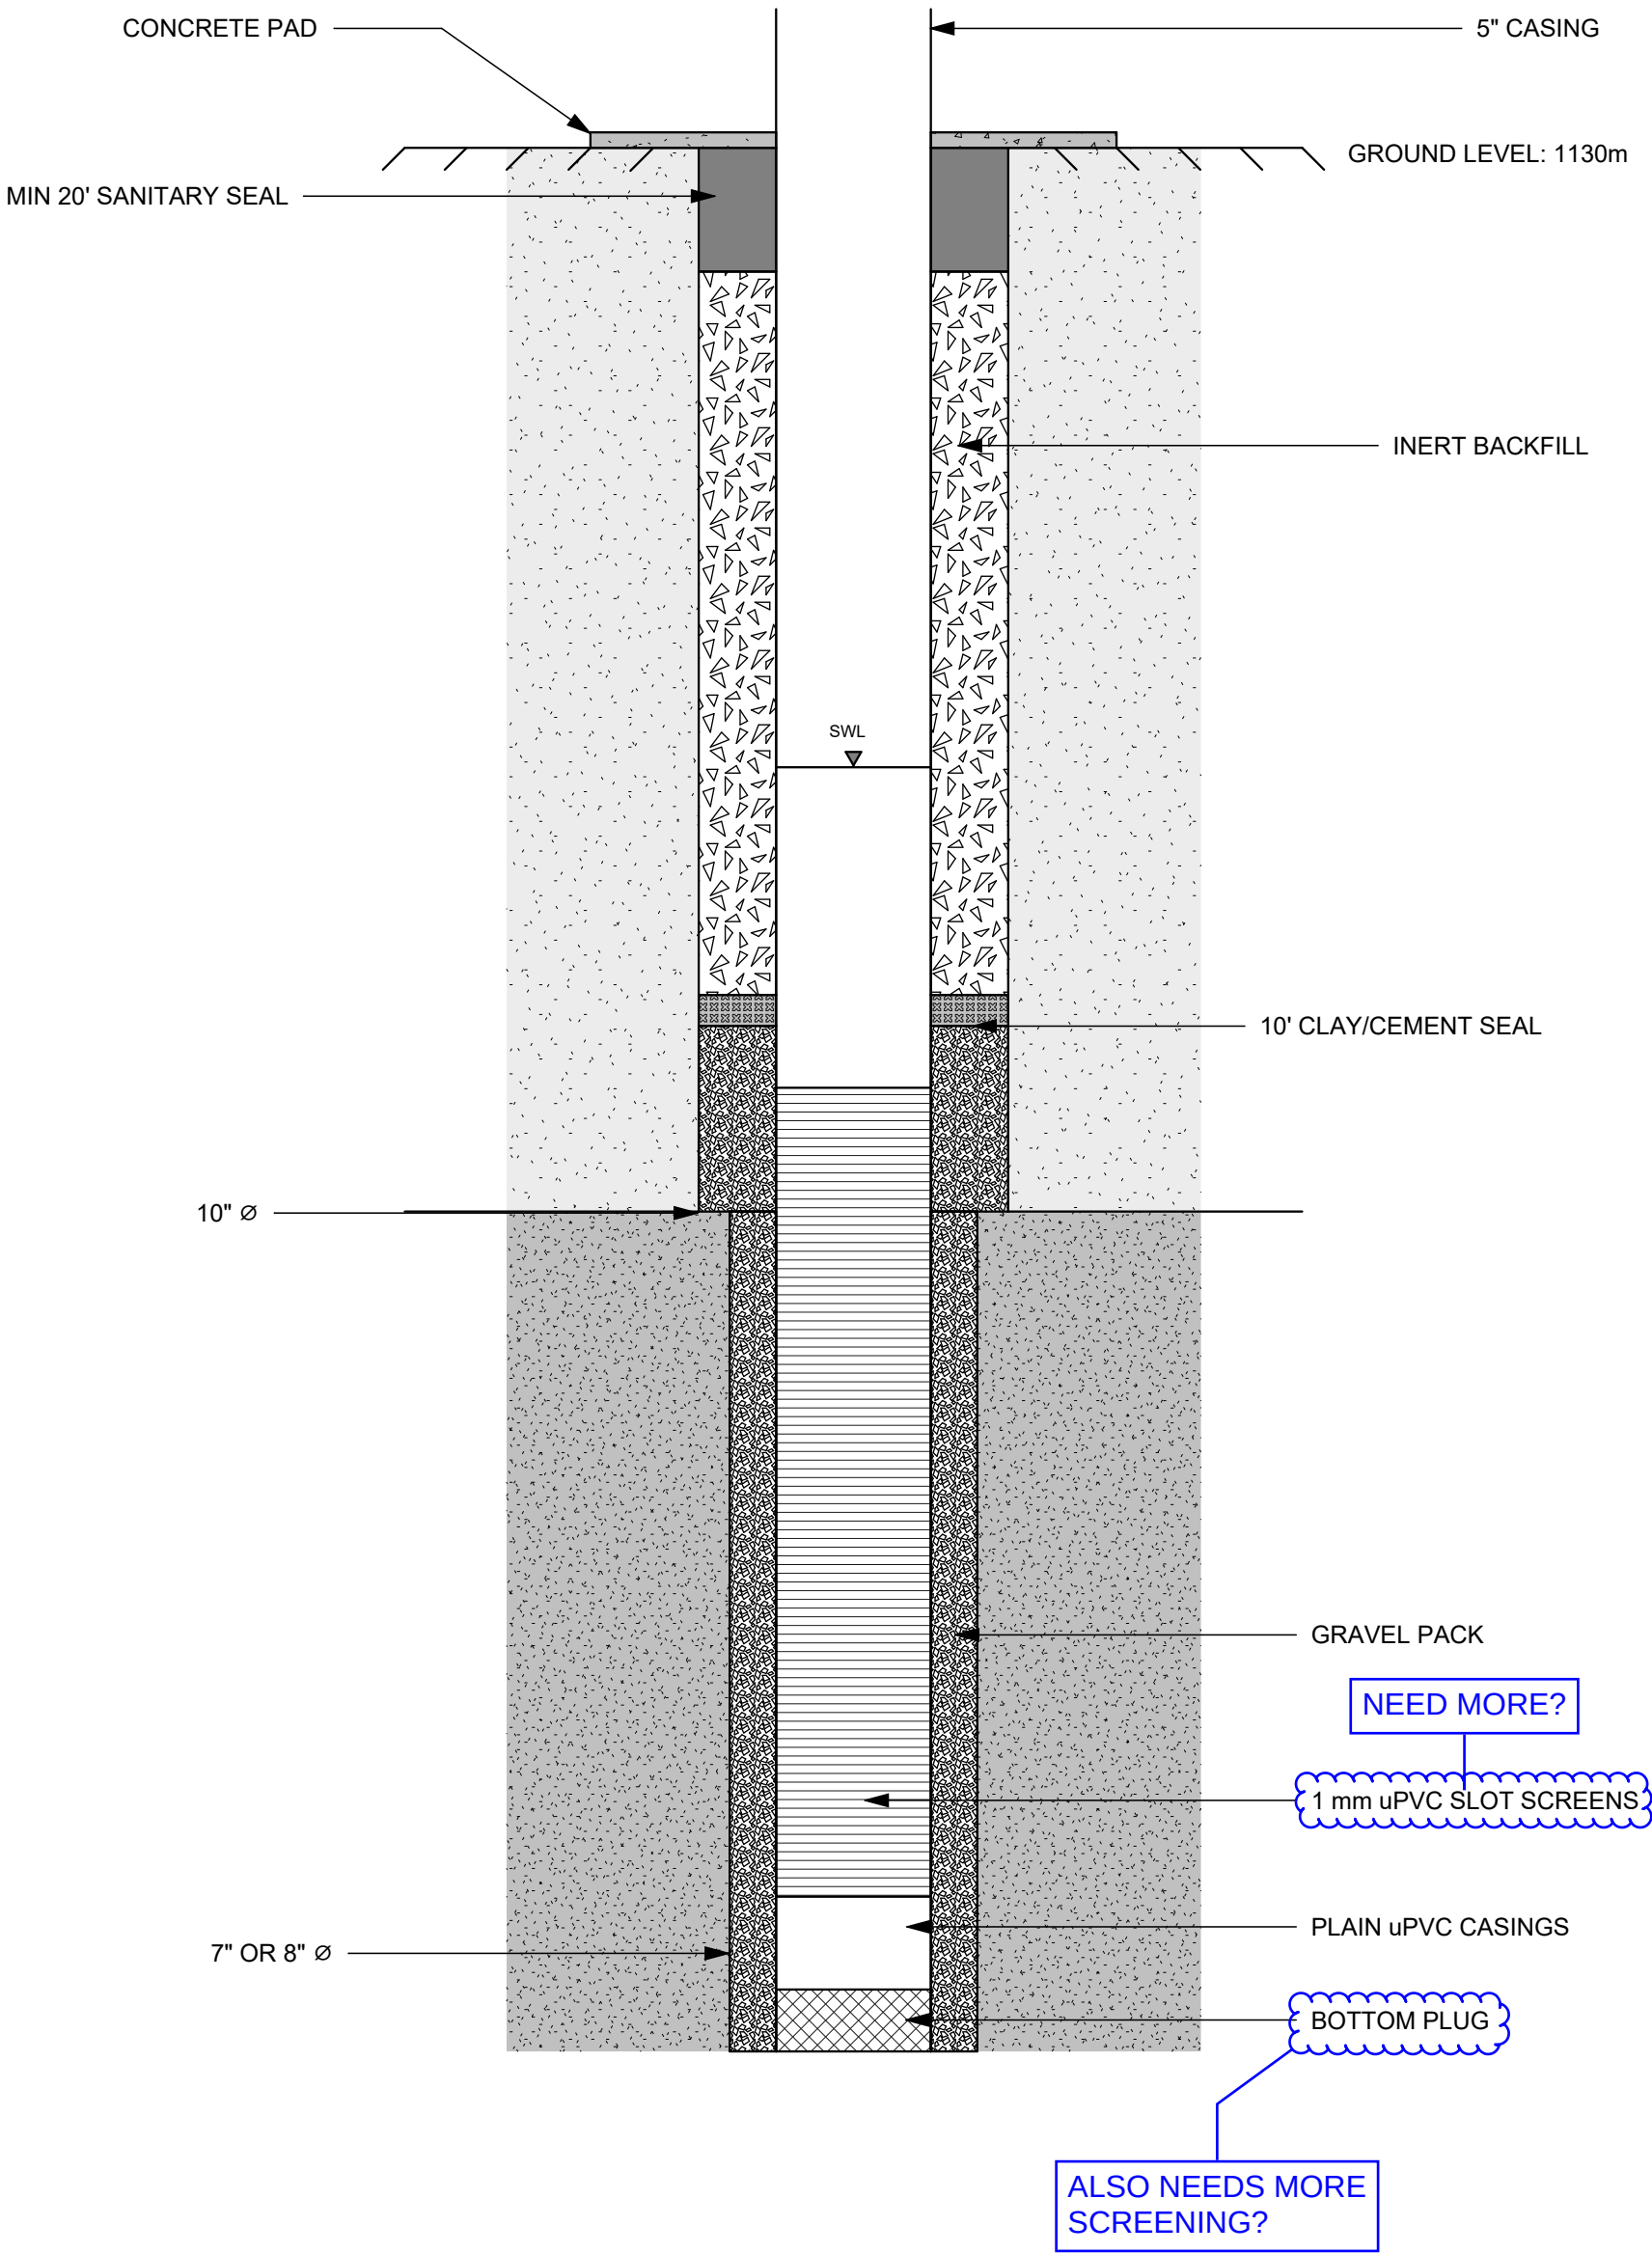

DRAFT

			UNIVERSITY OF KANSAS CHAPTER LAWRENCE, KS	REIC: E MOHAN	#####	UGANDA BUBAGO WATER SUPPLY BOREHOLE 1 DESIGN	DRAWING NO.: 001
				PROJECT LEAD: I DUNN	#####		
				PROJECT LEAD: A SETHI	#####		
				DRAWN BY: L HOPE	#####		
				ROLE	CHECK DATE		
DATE	REVISION						